


The chosen exterior concept. Materials and colour are indicative.

Sample · 10 marla modern home, Johar Town

10 marla · Johar Town, Lahore

Site plan

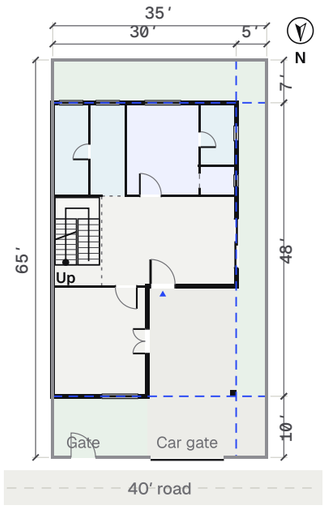


Area schedule	sq ft
Ground floor	1,440
First floor	1,203
Roof (stair tower)	119
Total covered	**2,762**
Plot	2,275
Ground coverage	63.3%
Floor area ratio	1:1.05
Height to parapet	27′

Cover and area schedule

Sample · 10 marla modern home, Johar Town

Plot 10 marla · 35′ × 65′	Location Johar Town, Lahore
Version Version 2 · 17 October 2026	Prepared by Naqsha, for the owner
Sheet A-000 · 1 of 6	Scale Not to scale

Design drawing for discussion and approval. Confirm all dimensions on site.

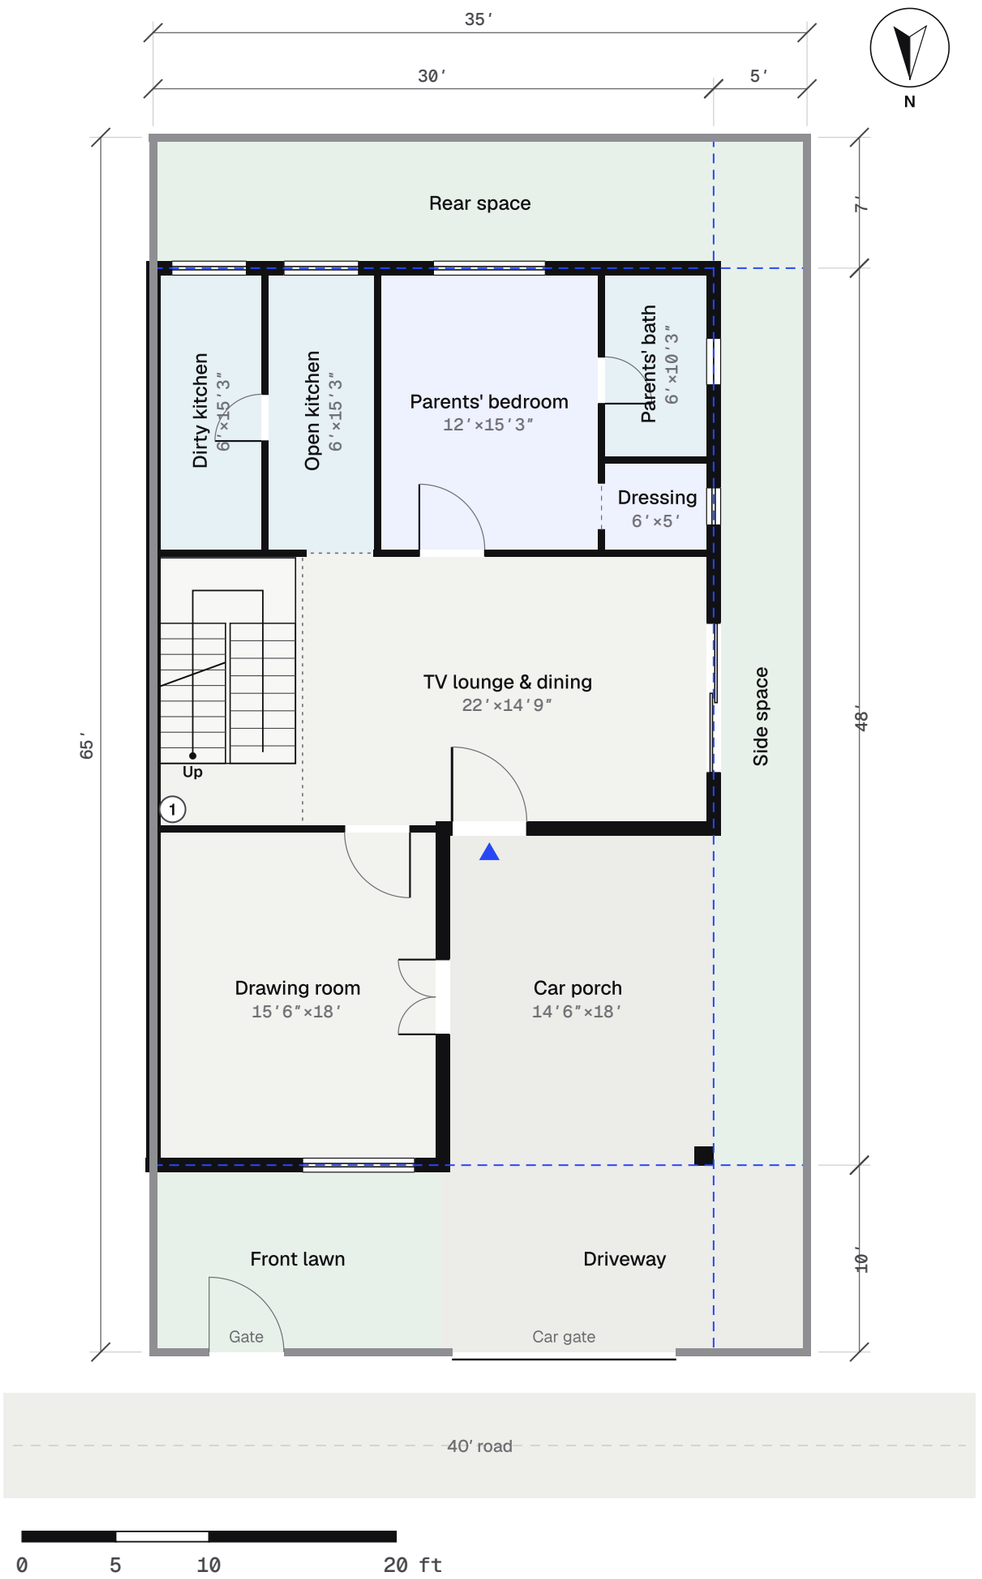

Ground floor

1,440 sq ft covered · scale 1:100

Room	Size	sq ft
TV lounge & dining	22′ × 14′9″	325
Drawing room	15′6″ × 18′	279
Car porch	14′6″ × 18′	261
Parents' bedroom	12′ × 15′3″	183
① Stair hall	8′ × 14′9″	118
Dirty kitchen	6′ × 15′3″	92
Open kitchen	6′ × 15′3″	92
Parents' bath	6′ × 10′3″	62
Parents' dressing	6′ × 5′	30


Setback (building line)

Ground floor plan

Sample · 10 marla modern home, Johar Town

Plot 10 marla · 35′ × 65′	Location Johar Town, Lahore
Version Version 2 · 17 October 2026	Prepared by Naqsha, for the owner
Sheet A-101 · 2 of 6	Scale 1:100 at A3

Design drawing for discussion and approval. Confirm all dimensions on site.

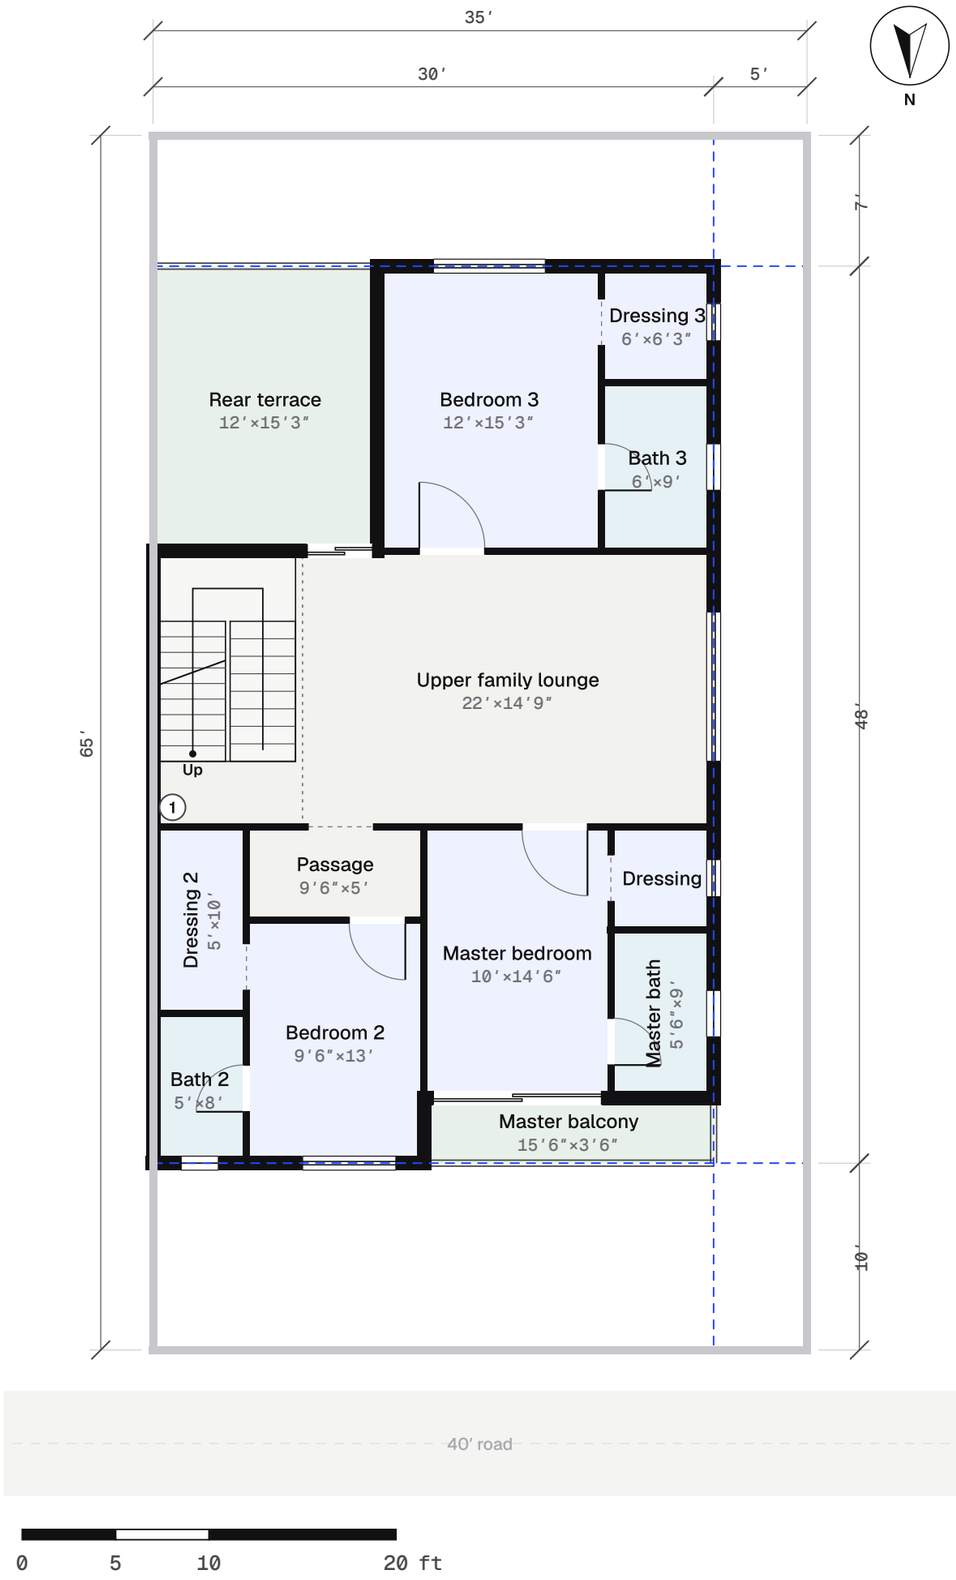

First floor

1,203 sq ft covered · scale 1:100

Room	Size	sq ft
Upper family lounge	22′ × 14′9″	325
Rear terrace	12′ × 15′3″	183
Bedroom 3	12′ × 15′3″	183
Master bedroom	10′ × 14′6″	145
Bedroom 2	9′6″ × 13′	124
① Stair hall	8′ × 14′9″	118
Master balcony	15′6″ × 3′6″	54
Bath 3	6′ × 9′	54
Dressing 2	5′ × 10′	50
Master bath	5′6″ × 9′	50
Passage	9′6″ × 5′	48
Bath 2	5′ × 8′	40
Dressing 3	6′ × 6′3″	38
Master dressing	5′6″ × 5′6″	30


----- Setback (building line)

First floor plan

Sample · 10 marla modern home, Johar Town

Plot 10 marla · 35′ × 65′	Location Johar Town, Lahore
Version Version 2 · 17 October 2026	Prepared by Naqsha, for the owner
Sheet A-102 · 3 of 6	Scale 1:100 at A3

Design drawing for discussion and approval. Confirm all dimensions on site.

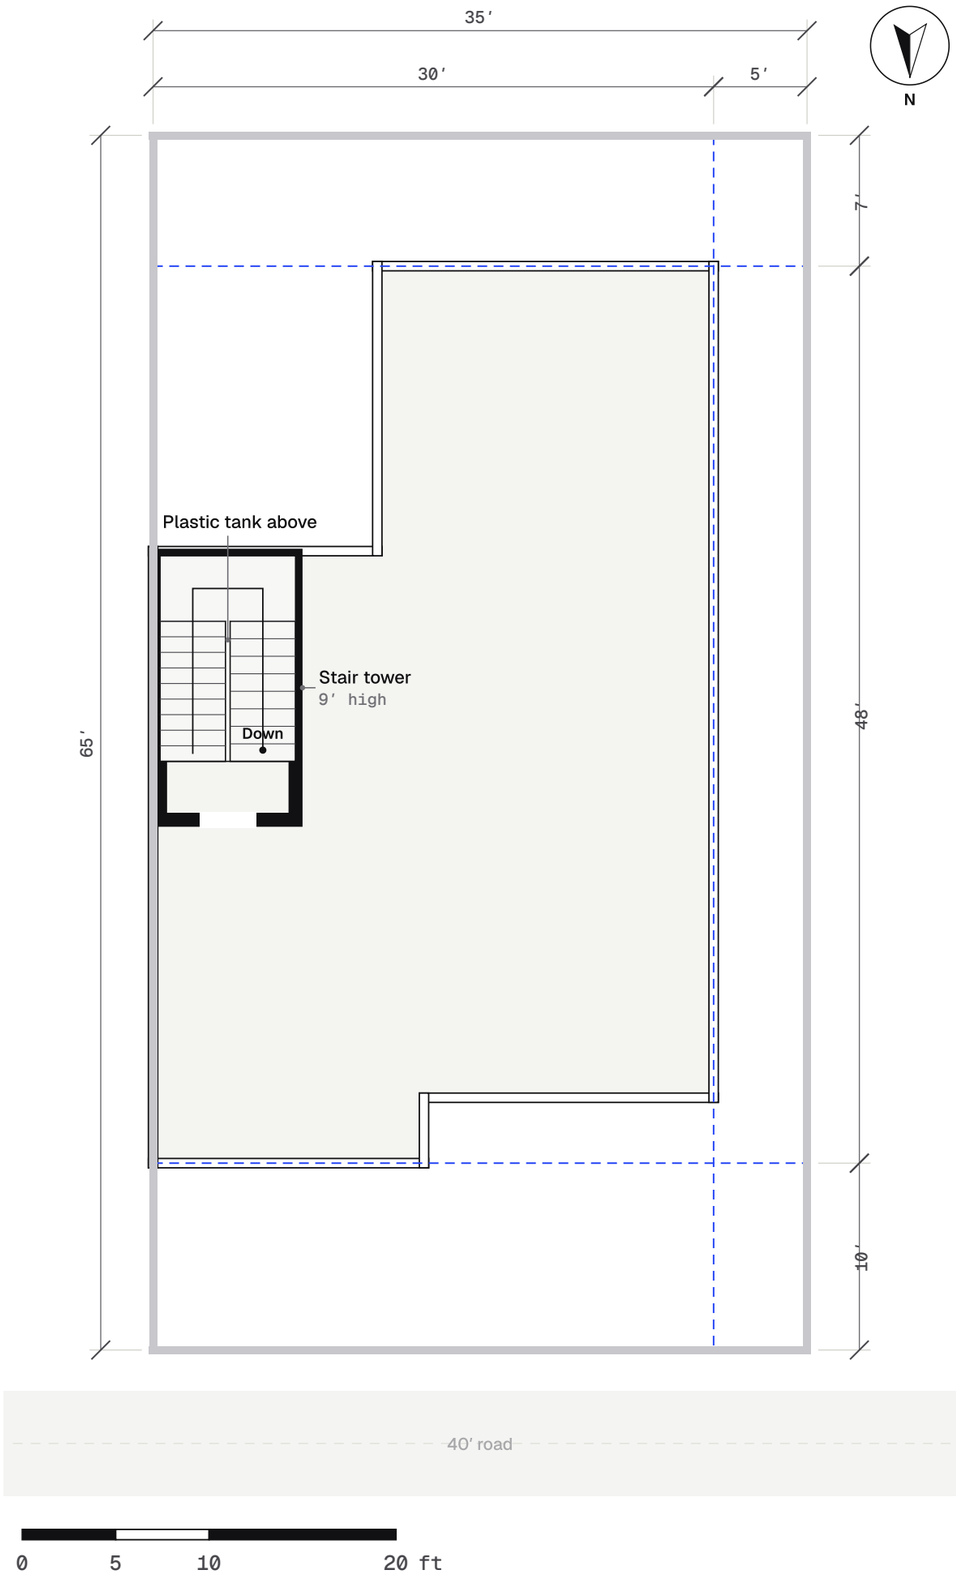

Roof

119 sq ft covered (stair tower) · scale 1:100

On the roof	Size	sq ft
Stair tower (mumty), 9′ high	8′ × 14′11″	119
Water tank, plastic	6′ × 6′	36

----- Setback (building line)

Roof plan

Sample · 10 marla modern home, Johar Town

Plot 10 marla · 35′ × 65′	Location Johar Town, Lahore
Version Version 2 · 17 October 2026	Prepared by Naqsha, for the owner
Sheet A-103 · 4 of 6	Scale 1:100 at A3

Design drawing for discussion and approval. Confirm all dimensions on site.

LDA rules · 36 pass

- Front setback (building line)
  `10′ (min 10′)`
- Rear setback
  `7′ (min 7′)`
- Side space
  `1 side (1 required)`
- Building within setbacks
  All rooms, porches and balconies sit inside the building line.
- Ground coverage
  `63.3% (max 70%)`
- Floor area ratio
  `1:1.05 (max 1:2.8)`
- Building height
  `27′ (max 45′)`
- Number of storeys
  `2 storeys (max 3)`
- Mumty (stair tower) height
  `9′ (max 9′6″)`
- Roof parapet
  `3′6″ (min 2′9″)`
- Boundary wall height
  `7′ (max 7′)`
- Drawing room size
  `279 sq ft (min 100 sq ft)`
- Drawing room daylight
  `30 sq ft of glass (22 sq ft needed)`
- TV lounge & dining size
  `324 sq ft (min 100 sq ft)`
- TV lounge & dining daylight
  `60 sq ft of glass (26 sq ft needed)`
- Dirty kitchen size
  `92 sq ft (min 50 sq ft)`
- Dirty kitchen daylight
  `18 sq ft of glass (7.3 sq ft needed)`
- Open kitchen size
  `92 sq ft (min 50 sq ft)`
- Open kitchen daylight
  `18 sq ft of glass (7.3 sq ft needed)`
- Parents' bedroom size
  `183 sq ft (min 100 sq ft)`
- Parents' bedroom daylight
  `27 sq ft of glass (15 sq ft needed)`
- Parents' bath ventilation
  `3.8 sq ft opening (2 sq ft needed)`
- Bedroom 2 size
  `124 sq ft (min 100 sq ft)`
- Bedroom 2 daylight
  `25 sq ft of glass (9.9 sq ft needed)`
- Bath 2 ventilation
  `3 sq ft opening (2 sq ft needed)`
- Master bedroom size
  `145 sq ft (min 100 sq ft)`
- Master bedroom daylight
  `77 sq ft of glass (12 sq ft needed)`
- Master bath ventilation
  `3.8 sq ft opening (2 sq ft needed)`
- Upper family lounge size
  `324 sq ft (min 100 sq ft)`
- Upper family lounge daylight
  `62 sq ft of glass (26 sq ft needed)`
- Bedroom 3 size
  `183 sq ft (min 100 sq ft)`
- Bedroom 3 daylight
  `27 sq ft of glass (15 sq ft needed)`
- Bath 3 ventilation
  `3.8 sq ft opening (2 sq ft needed)`
- Ground → first stair
  19 risers of 6.95 in, 3′6″ wide, 10 in treads, 2 flights of up to 10 risers.
- First → roof stair
  19 risers of 6.95 in, 3′6″ wide, 10 in treads, 2 flights of up to 10 risers.
- Overhead water tank
  Overhead water tank on the roof.

Livable home · 10 pass · 5 to check

- Door width — **Check**
  `2′6″ (limit 3′)`
  The door between Dirty Kitchen and Open Kitchen is 2′6″ wide; 3′ is the comfortable minimum here.
- Roof kept clear for solar
  `64% clear (min 55%)`
  64% kept clear (min 55%): about 772 sq ft for panels, roughly 11 kW.
- Bath over a dry room — **Check**
  Bath 2 sits over Drawing Room: leaks and drain pipes would run through its ceiling.
- Rooms are independent
  Bedrooms open only onto a corridor, lobby, lounge, balcony or their own bath; no two bedrooms share a balcony; a dressing opens only into its own bedroom; baths have one door.
- Every room has a proper way in
  Every room is reached through circulation, never through a bedroom or bath, and the family reaches the lounge without crossing the drawing room.
- Stairs reach every floor and the roof
  One stacked stair climbs to every floor and the roof, with a 3 ft landing at the foot and the top.
- The roof door is at the top of the stair
  The stair tower covers the stair and its top landing, and its door opens beside that landing.
- Doors and windows fit their walls
  Every door and window sits on a wall the two rooms share, on the same floor, and fits inside it.
- Rooms match your brief
  The bedrooms, baths and rooms on each floor follow the brief.
- Architect's review: needs a change — **Check**
  Placing the Open Kitchen and Dirty Kitchen side-by-side makes both rooms 6 ft wide by 15.25 ft deep—long, narrow tunnels where a 2 ft counter leaves barely 3.5 ft of passage and no room for two people to pass or open appliances. Suggested: Divide the 12 x 15.25 ft kitchen zone front-to-back instead of left-to-right: place a 12 x 6.5 ft Dirty Kitchen at the back against the Rear Space and a 12 x 8.75 ft Open Kitchen in front opening to the TV Lounge & Dining, connected by a 3 ft door.

Passes all 36 LDA checks; 5 livable points to check

LDA Building and Zoning Regulations · 10 marla and above but less than 1 kanal · 35′ × 65′ plot, front faces north

Pass · Check · Fix

Compliance report

Sample · 10 marla modern home, Johar Town

Plot	Location
10 marla · 35′ × 65′	Johar Town, Lahore
Version	Prepared by
Version 2 · 17 October 2026	Naqsha, for the owner
Sheet	Scale
A-900 · 5 of 6	Not to scale

Design drawing for discussion and approval. Confirm all dimensions on site.

- Architect's review — Check

  Bath 2 sits directly over the front-left corner of the Drawing Room, meaning soil and waste pipes will run through the formal guest ceiling and risk visible leaks. Suggested: Move Bath 2 to the back of Bedroom 2 against the Stair Hall wall so its plumbing drops down outside the main Drawing Room ceiling.

- Architect's review — Check

  There is no powder room on the ground floor, so Drawing Room guests must walk through the family TV Lounge and into the Parents' Bedroom to use a bathroom. Suggested: Tuck a 4 x 5 ft powder room under the high flight and landing of the Stair Hall, opening discreetly near the Drawing Room door.

- Every stair edge and void has a railing

  A 3'6" railing is built along every stair edge, void and balcony.

- Doors are clear of furniture

  Furniture keeps out of every door swing.

- A clear 3 ft path to every door

  Every passage is at least 3 ft wide.

Pass · Check · Fix

Compliance report, continued

Sample · 10 marla modern home, Johar Town

Plot	Location
10 marla · 35′ × 65′	Johar Town, Lahore
Version	Prepared by
Version 2 · 17 October 2026	Naqsha, for the owner
Sheet	Scale
A-901 · 6 of 6	Not to scale

Design drawing for discussion and approval. Confirm all dimensions on site.